


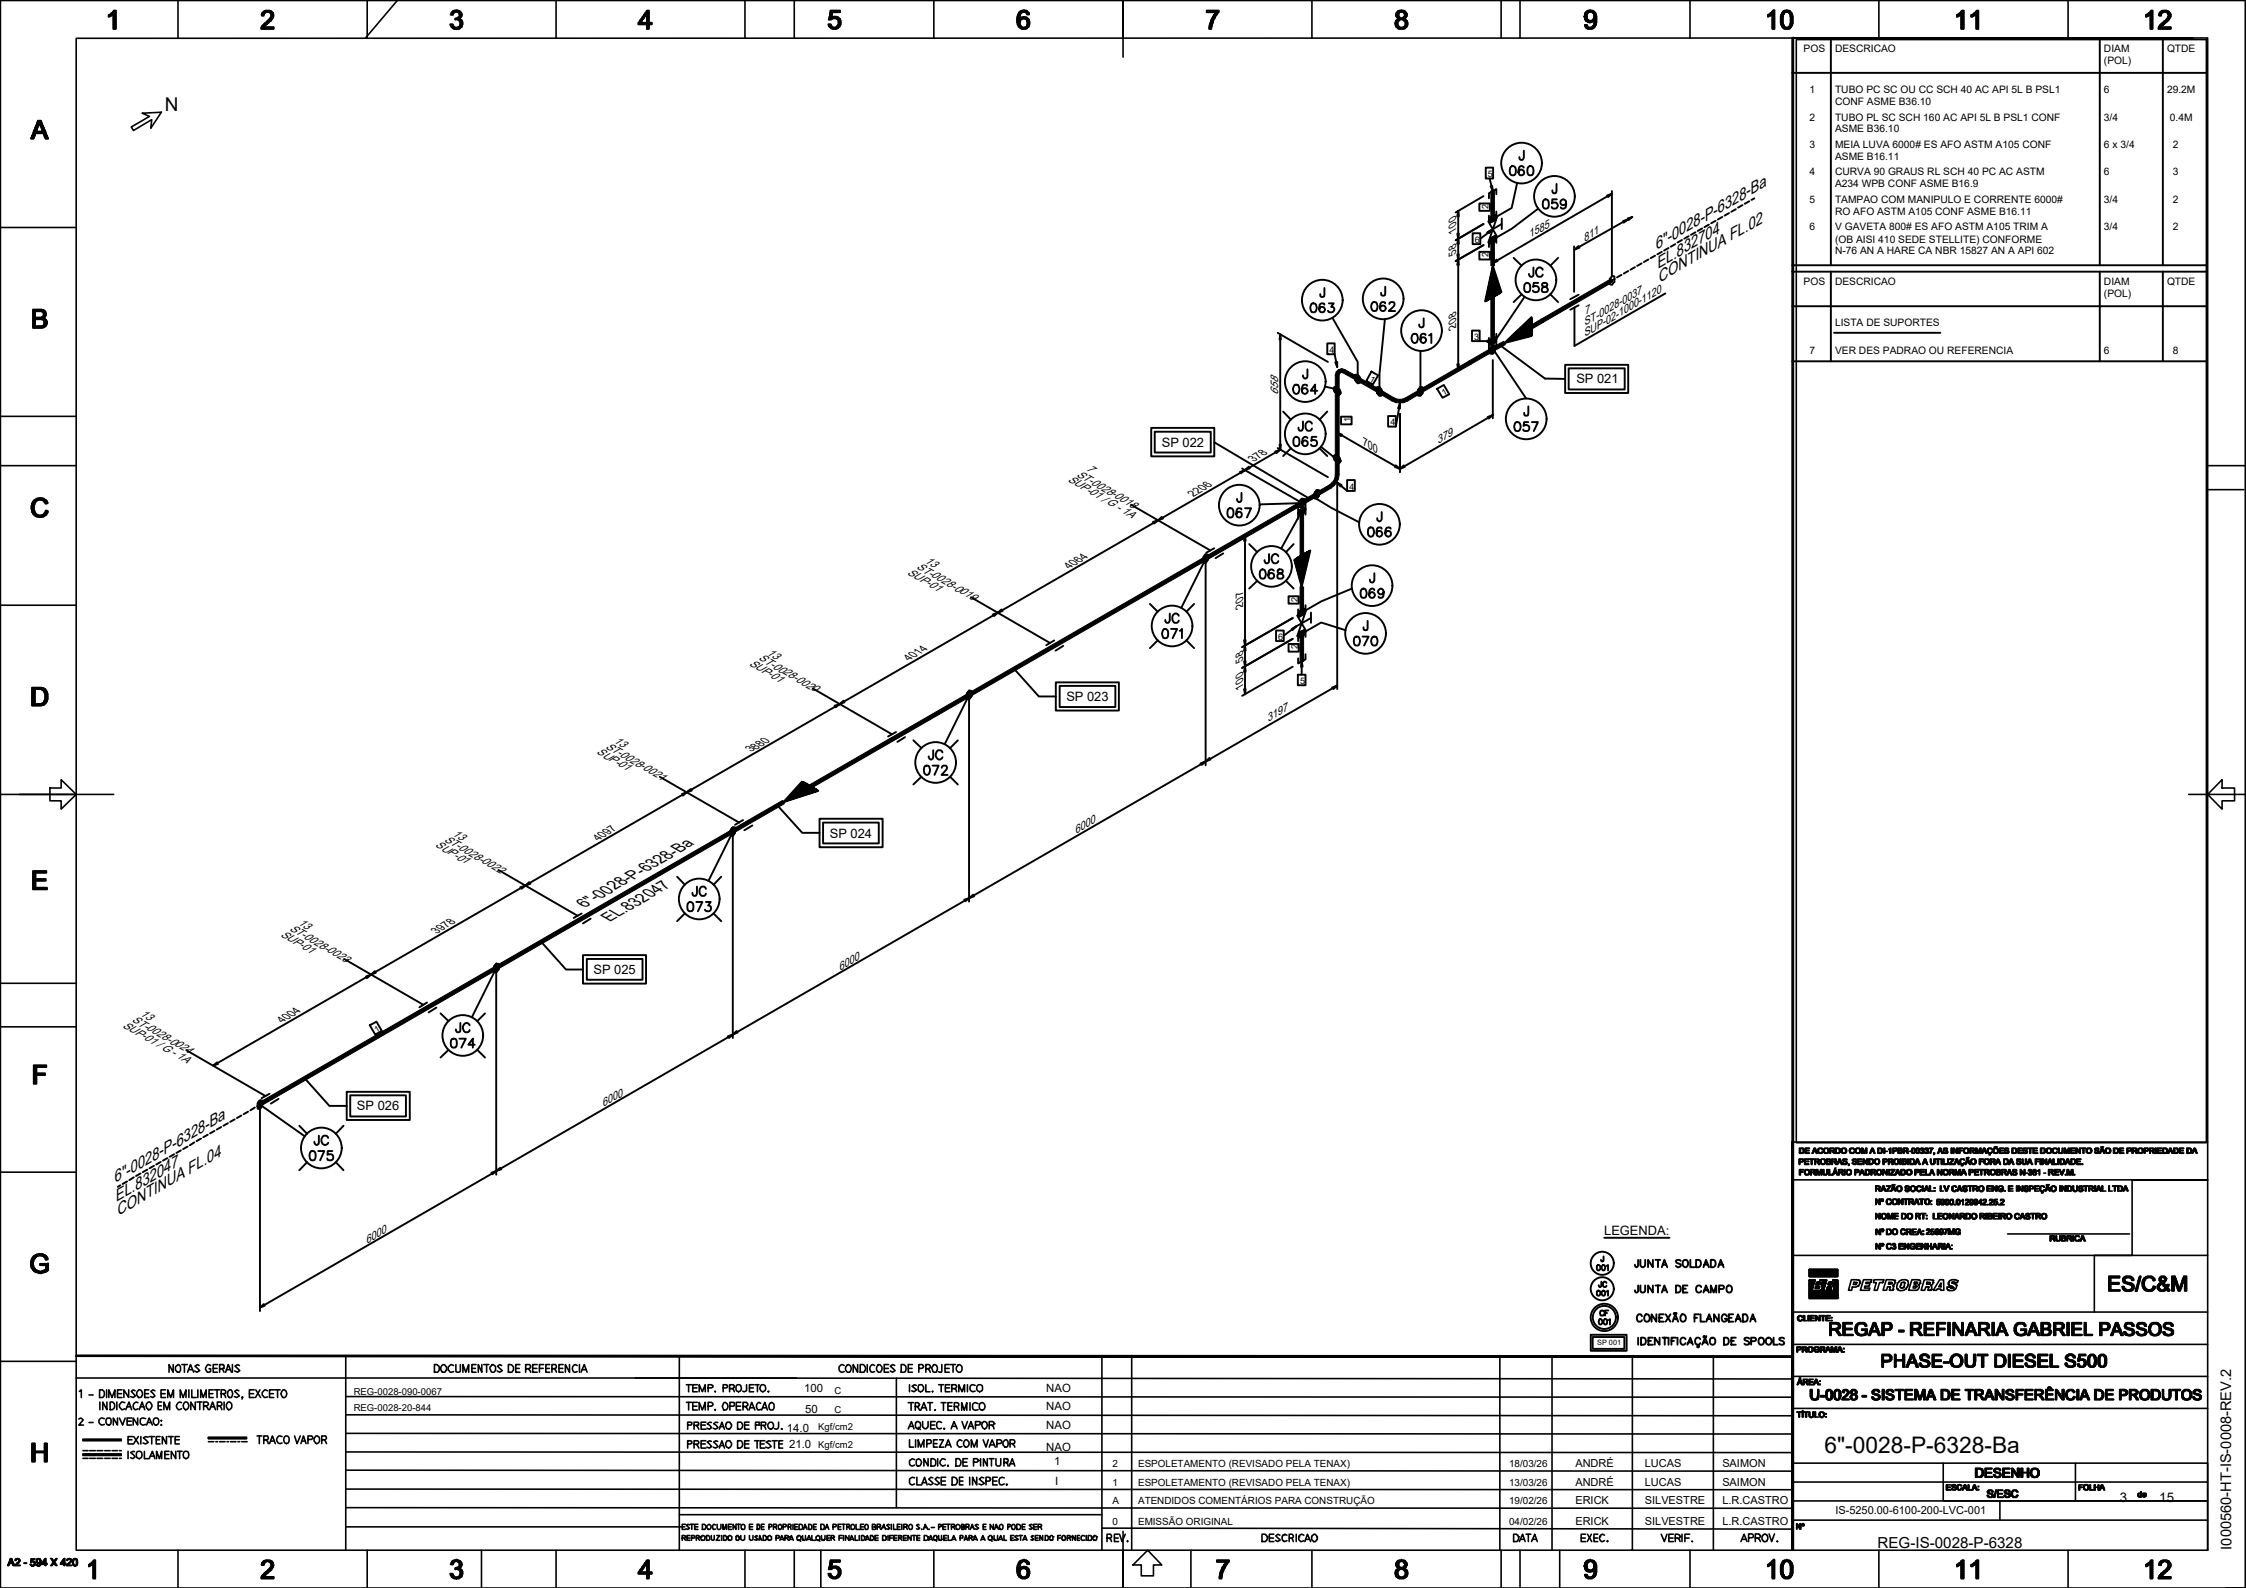

POS	DESCRIÇÃO	DIAM (POL)	QTDE
1	TUBO PC SC OU CC SCH 40 AC API 5L B PSL1 CONF ASME B36.10	6	29.2M
2	TUBO PL SC SCH 160 AC API 5L B PSL1 CONF ASME B36.10	3/4	0.4M
3	MEIA LULA 6000# ES AFO ASTM A105 CONF ASME B16.11	6 x 3/4	2
4	CURVA 90 GRAUS RL SCH 40 PC AC ASTM A234 WPB CONF ASME B16.9	6	3
5	TAMPAO COM MANIPULO E CORRENTE 6000# RO AFO ASTM A105 CONF ASME B16.11	3/4	2
6	V GAVETA 800# ES AFO ASTM A105 TRIM A (08 AISI 410 SEDE STELLITE) CONFORME N-76 AN A HARE CA NBR 15827 AN A API 602	3/4	2

POS	DESCRIÇÃO	DIAM (POL)	QTDE
LISTA DE SUPORTES			
7	VER DES PADRAO OU REFERENCIA	6	8

DE ACORDO COM A DI-IPBR-00387, AS INFORMAÇÕES DESTA DOCUMENTO SÃO DE PROPRIEDADE DA PETROBRAS, SENDO PROIBIDA A UTILIZAÇÃO FORA DA SUA FINALIDADE. FORMULÁRIO PRODUZIDO PELA NORMA PETROBRAS N-381 - REV.04

RAZÃO SOCIAL: LV CASTRO ENG. E INSPEÇÃO INDUSTRIAL LTDA
Nº CONTRATO: 080.0128842.25.2
NOME DO RT: LEONARDO FERRERO CASTRO
Nº DO CREA: 25887043
Nº CS ENGENHARIA: _____ RUBRICA

PETROBRAS **ES/C&M**

CLIENTE: **REGAP - REFINARIA GABRIEL PASSOS**

PROGRAMA: **PHASE-OUT DIESEL S500**

ÁREA: **U-0028 - SISTEMA DE TRANSFERÊNCIA DE PRODUTOS**

TÍTULO: **6"-0028-P-6328-Ba**

DESENHO: _____ ESEC: _____ FOLHA: 3 de 15

IS-5250.00-6100-200-LVC-001

Nº _____ REG-IS-0028-P-6328

NOTAS GERAIS		DOCUMENTOS DE REFERENCIA		CONDICOES DE PROJETO							
1 - DIMENSÕES EM MILÍMETROS, EXCETO INDICAÇÃO EM CONTRÁRIO		REG-0028-090-0067		TEMP. PROJETO	100 C	ISOL. TERMICO	NAO				
2 - CONVENÇÃO:		REG-0028-20-844		TEMP. OPERAÇÃO	50 C	TRAT. TERMICO	NAO				
— EXISTENTE — TRACO VAPOR				PRESSAO DE PROJ.	14.0 Kgfl/cm2	AQUEC. A VAPOR	NAO				
— ISOLAMENTO				PRESSAO DE TESTE	21.0 Kgfl/cm2	LIMPEZA COM VAPOR	NAO				
				CONDIC. DE PINTURA	1	2	ESPOLETAMENTO (REVISADO PELA TENAX)	18/03/26	ANDRÉ	LUCAS	SAIMON
				CLASSE DE INSPEC.	I	1	ESPOLETAMENTO (REVISADO PELA TENAX)	13/03/26	ANDRÉ	LUCAS	SAIMON
						A	ATENDIDOS COMENTÁRIOS PARA CONSTRUÇÃO	19/02/26	ERICK	SILVESTRE	L.R.CASTRO
						0	EMISSÃO ORIGINAL	04/02/26	ERICK	SILVESTRE	L.R.CASTRO
						REV.	DESCRIÇÃO	DATA	EXEC.	VERIF.	APROV.