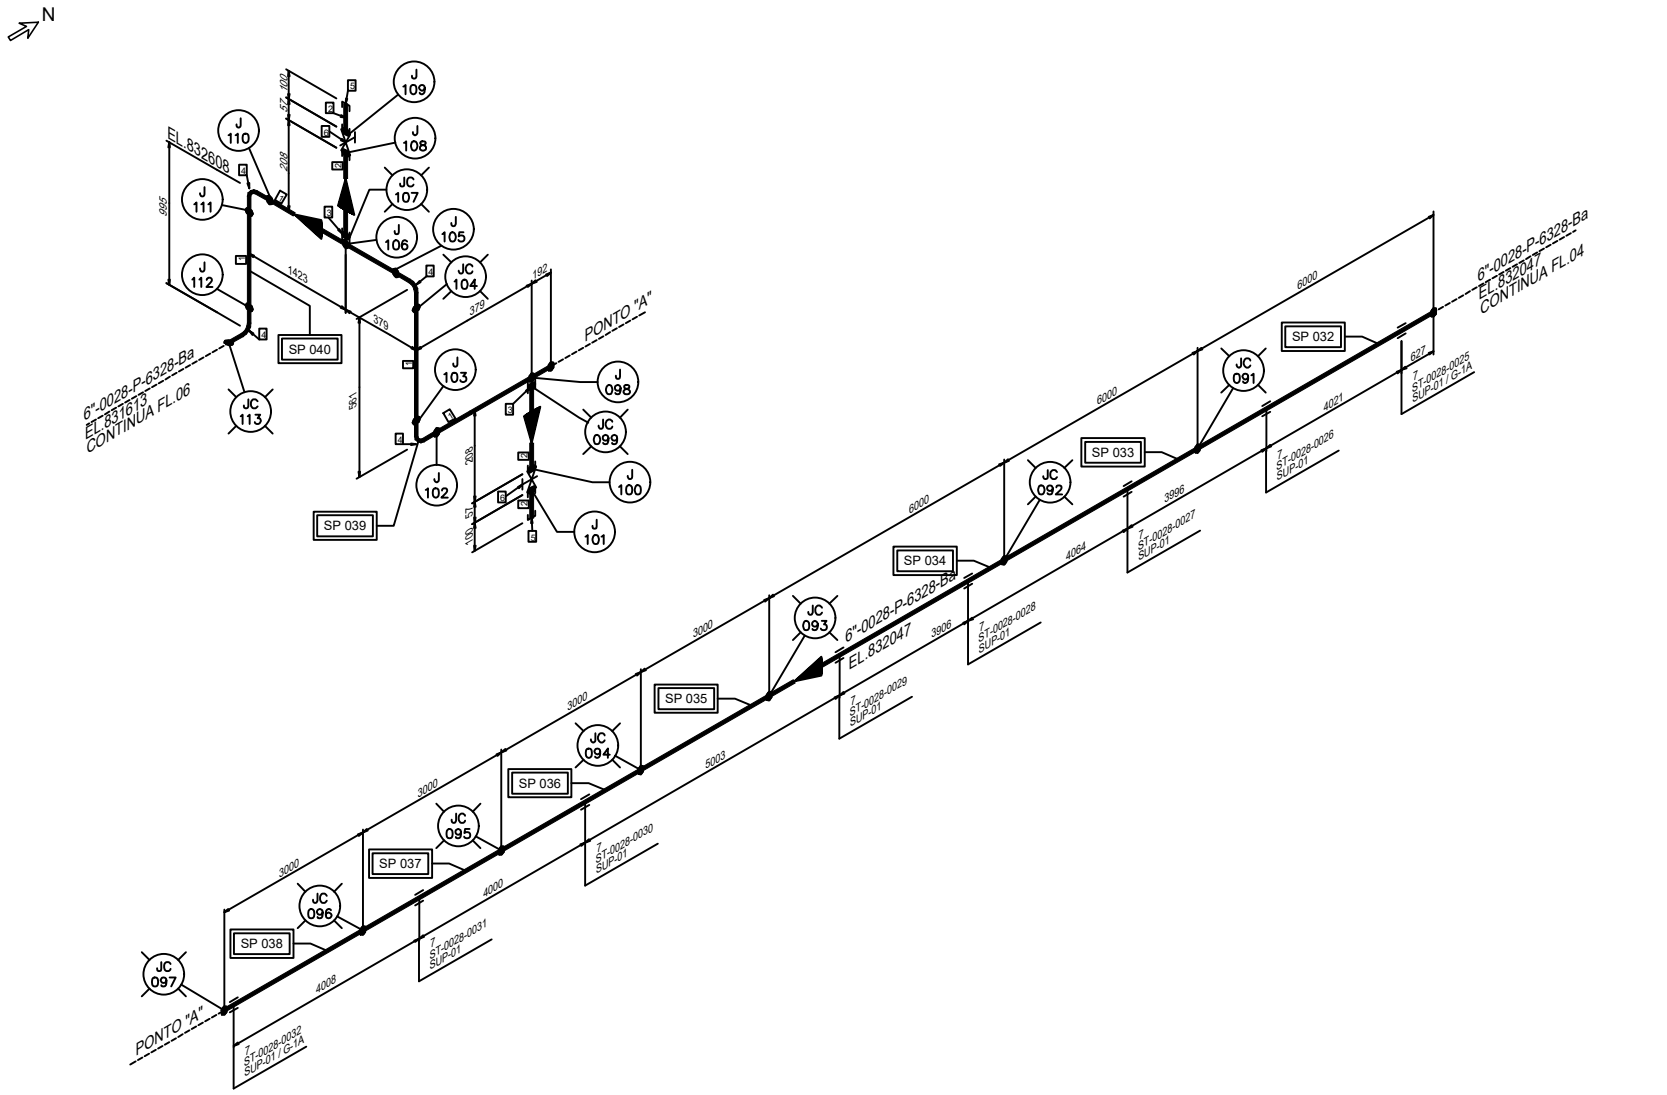

LEGENDA:

- JUNTA SOLDADA
- JUNTA DE CAMPO
- CONEXÃO FLANGEADA
- SP 001 IDENTIFICAÇÃO DE SPOOLS

POS	DESCRICAO	DIAM (POL)	QTDE
1	TUBO PC SC OU CC SCH 40 AC API 5L B PSL1 CONF ASME B36.10	6	32.4M
2	TUBO PL SC SCH 160 AC API 5L B PSL1 CONF ASME B36.10	3/4	0.4M
3	MEIA LUVA 6000# ES AFO ASTM A105 CONF ASME B16.11	6 x 3/4	2
4	CURVA 90 GRAUS RL SCH 40 PC AC ASTM A234 WPB CONF ASME B16.9	6	4
5	TAMPAO COM MANIPULO E CORRENTE 6000# RO AFO ASTM A105 CONF ASME B16.11	3/4	2
6	V GAVETA 800# ES AFO ASTM A105 TRIM A (OB AISI 410 SEDE STELLITE) CONFORME N-76 AN A HARE CA NBR 15827 AN A API 602	3/4	2

POS	DESCRICAO	DIAM (POL)	QTDE
	LISTA DE SUPORTES		
7	VER DES PADRAO OU REFERENCIA	6	8

DE ACORDO COM A DI-1PBR-00397, AS INFORMAÇÕES DESTE DOCUMENTO SÃO DE PROPRIEDADE DA PETROBRAS, SENDO PROIBIDA A UTILIZAÇÃO FORA DA SUA FINALIDADE.
FORMULÁRIO PADRONIZADO PELA NORMA PETROBRAS N-381 - REV.M.

RAZÃO SOCIAL: LV CASTRO ENG. E INSPEÇÃO INDUSTRIAL LTDA
Nº CONTRATO: 0800.0123942.25.2
NOME DO RT: LEONARDO RIBEIRO CASTRO
Nº DO CREA: 356870/D
Nº CS ENGENHARIA:
RUBRICA

PETROBRAS | ES/C&M

CLIENTE: REGAP - REFINARIA GABRIEL PASSOS
PROGRAMA: PHASE-OUT DIESEL S500
ÁREA: U-0028 - SISTEMA DE TRANSFERÊNCIA DE PRODUTOS
TÍTULO: 6"-0028-P-6328-Ba

DESENHO
ESCALA: S/ESC FOLHA 5 de 15
IS-5250.00-6100-200-LVC-001
Nº REG-IS-0028-P-6328

NOTAS GERAIS	DOCUMENTOS DE REFERENCIA
1 - DIMENSOES EM MILIMETROS, EXCETO INDICACAO EM CONTRARIO	REG-0028-090-0067
2 - CONVENCAO:	REG-0028-20-844
EXISTENTE ═══ TRACO VAPOR ═══ ISOLAMENTO	

CONDICOES DE PROJETO			
TEMP. PROJETO.	100 C	ISOL. TERMICO	NAO
TEMP. OPERACAO	50 C	TRAT. TERMICO	NAO
PRESSAO DE PROJ.	14.0 Kgf/cm2	AQUEC. A VAPOR	NAO
PRESSAO DE TESTE	21.0 Kgf/cm2	LIMPEZA COM VAPOR	NAO
		CONDIC. DE PINTURA	1
		CLASSE DE INSPEC.	I

REV.	DESCRICAO	DATA	EXEC.	VERIF.	APROV.
2	ESPOLETAMENTO (REVISADO PELA TENAX)	18/03/26	ANDRÉ	LUCAS	SAIMON
1	ESPOLETAMENTO (REVISADO PELA TENAX)	16/03/26	ANDRÉ	LUCAS	SAIMON
A	ATENDIDOS COMENTÁRIOS PARA CONSTRUÇÃO	19/02/26	ERICK	SILVESTRE	L.R.CASTRO
0	EMISSÃO ORIGINAL	04/02/26	ERICK	SILVESTRE	L.R.CASTRO

ESTE DOCUMENTO E DE PROPRIEDADE DA PETROLEO BRASILEIRO S.A.- PETROBRAS E NAO PODE SER REPRODUZIDO OU USADO PARA QUALQUER FINALIDADE DIFERENTE DAQUELA PARA A QUAL ESTA SENDO FORNECIDO

I000560-HT-IS-0010-REV.1

A2 - 594 X 420