


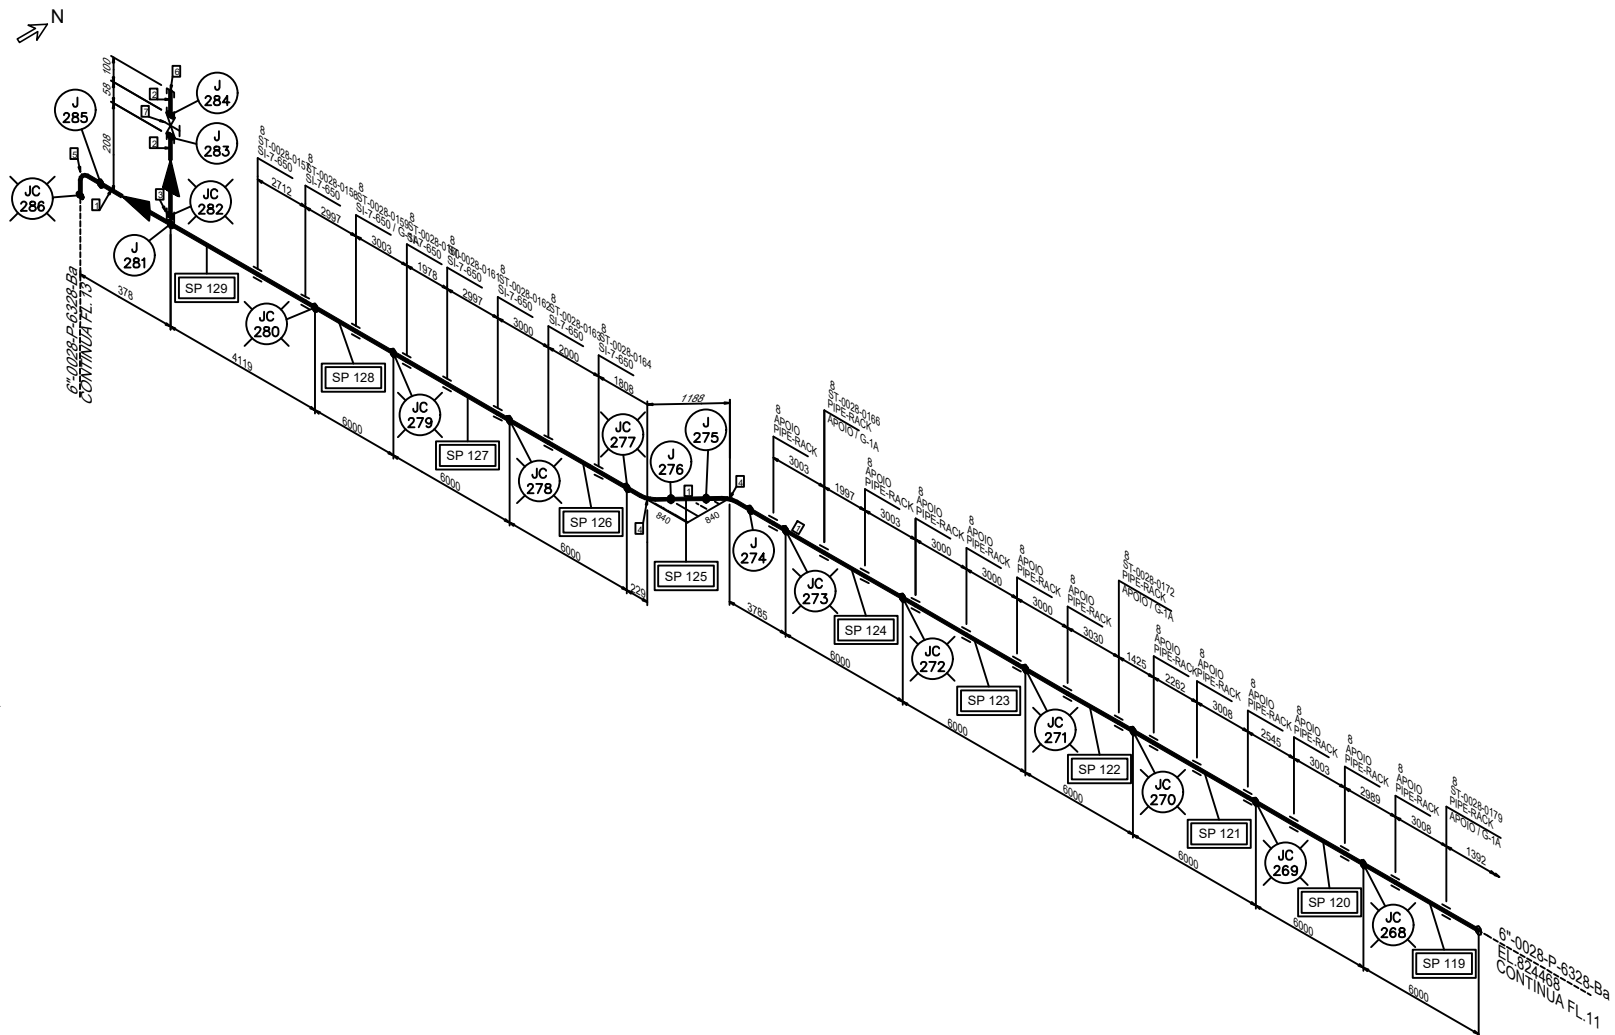

POS	DESCRICAO	DIAM (POL)	QTDE
1	TUBO PC SC OU CC SCH 40 AC API 5L B PSL 1 CONF ASME B36.10	6	83.1M
2	TUBO PL SC SCH 160 AC API 5L B PSL 1 CONF ASME B36.10	3/4	0.2M
3	MEIA LULA 6000# ES AFO ASTM A105 CONF ASME B16.11	6 x 3/4	1
4	CURVA 45 GRAUS RL SCH 40 PC AC ASTM A234 WPB CONF ASME B16.9	6	2
5	CURVA 90 GRAUS RL SCH 40 PC AC ASTM A234 WPB CONF ASME B16.9	6	1
6	TAMPAO COM MANIPULO E CORRENTE 6000# RO AFO ASTM A105 CONF ASME B 16.11	3/4	1
7	V GAUETA 800# ES AFO ASTM A105 TRIM A (OB AISI 410 SEDE STELLITE) CONFORME N-76 AN A HARE CA NBR 15827 AN API 602	3/4	1
POS	DESCRICAO	DIAM (POL)	QTDE
	<u>LISTA DE SUPORTES</u>		
8	VER DES PADRAO OU REFERENCIA	6	23

DE ACORDO COM A DI-IPBR-00037, AS INFORMAÇÕES DESTES DOCUMENTOS SÃO DE PROPRIEDADE DA PETROBRAS, SENDO PROIBIDA A UTILIZAÇÃO FORA DA SUA FINALIDADE. FORMULÁRIO PADRONIZADO PELA NORMA PETROBRAS N-361 - REV.31	
RAZÃO SOCIAL: LV CASTRO ENG. E INSPEÇÃO INDUSTRIAL LTDA Nº CONTRATO: 0880.0128042.26.2 NOME DO RT: LEONARDO RIBEIRO CASTRO Nº DO CREA: 26887/MG Nº C3 ENGENHARIA:	RUBRICA _____

PETROBRAS **ES/C&M**

CLIENTE: REGAP - REFINARIA GABRIEL PASSOS

PROGRAMA:	PHASE-OUT DIESEL S500
-----------	-----------------------

AREA: U-0028 - SISTEMA DE TRANSFERÊNCIA DE PRODUTOS

6"-0028-P-6328-Ba

		DESENHO	
		ESCALA: S/FSC	FOLHA 12 de 15
IS-5250.00-6100-200-LVC-001			

REG-IS-0028-P-6328

NOTAS GERAIS		DOCUMENTOS DE REFERENCIA		CONDICOES DE PROJETO											
1 - DIMENSÕES EM MILÍMETROS, EXCETO INDICAÇÃO EM CONTRÁRIO 2 - CONVENÇÃO: EXISTENTE TRACO VAPOR ISOLAMENTO	REG-0028-090-0067	TEMP. PROJETO.	100 C	ISOL. TERMICO	NAO										
	REG-0028-20-844	TEMP. OPERACAO	50 C	TRAT. TERMICO	NAO										
		PRESSAO DE PROJ.	14,0 Kgf/cm2	AQUEC. A VAPOR	NAO										
		PRESSAO DE TESTE	21,0 Kgf/cm2	LIMPEZA COM VAPOR	NAO										
				CONDIC. DE PINTURA	1										
				CLASSE DE INSPEC.	I	1	ESPOLETAMENTO (REVISAO PELA TENAX)	23/03/26	ANDRÉ	LUCAS	SAIMON				
						A	ATENDIDOS COMENTÁRIOS PARA CONSTRUÇÃO	19/02/26	ERICK	SILVESTRE	L.R.CASTR				
						0	EMISSÃO ORIGINAL	04/02/26	ERICK	SILVESTRE	L.R.CASTR				
			ESTE DOCUMENTO É DE PROPRIEDADE DA PETROLIO BRASILEIRO S.A. - PETROBRAS E NAO PODE SER REPRODUZIDO OU USADO PARA QUALQUER FINALIDADE DIFERENTE DAQUELA PARA A QUAL ESTA SENDO FORNECIDO			REV.	DESCRICAO	DATA	EXEC.	VERIF.	APROV.				