


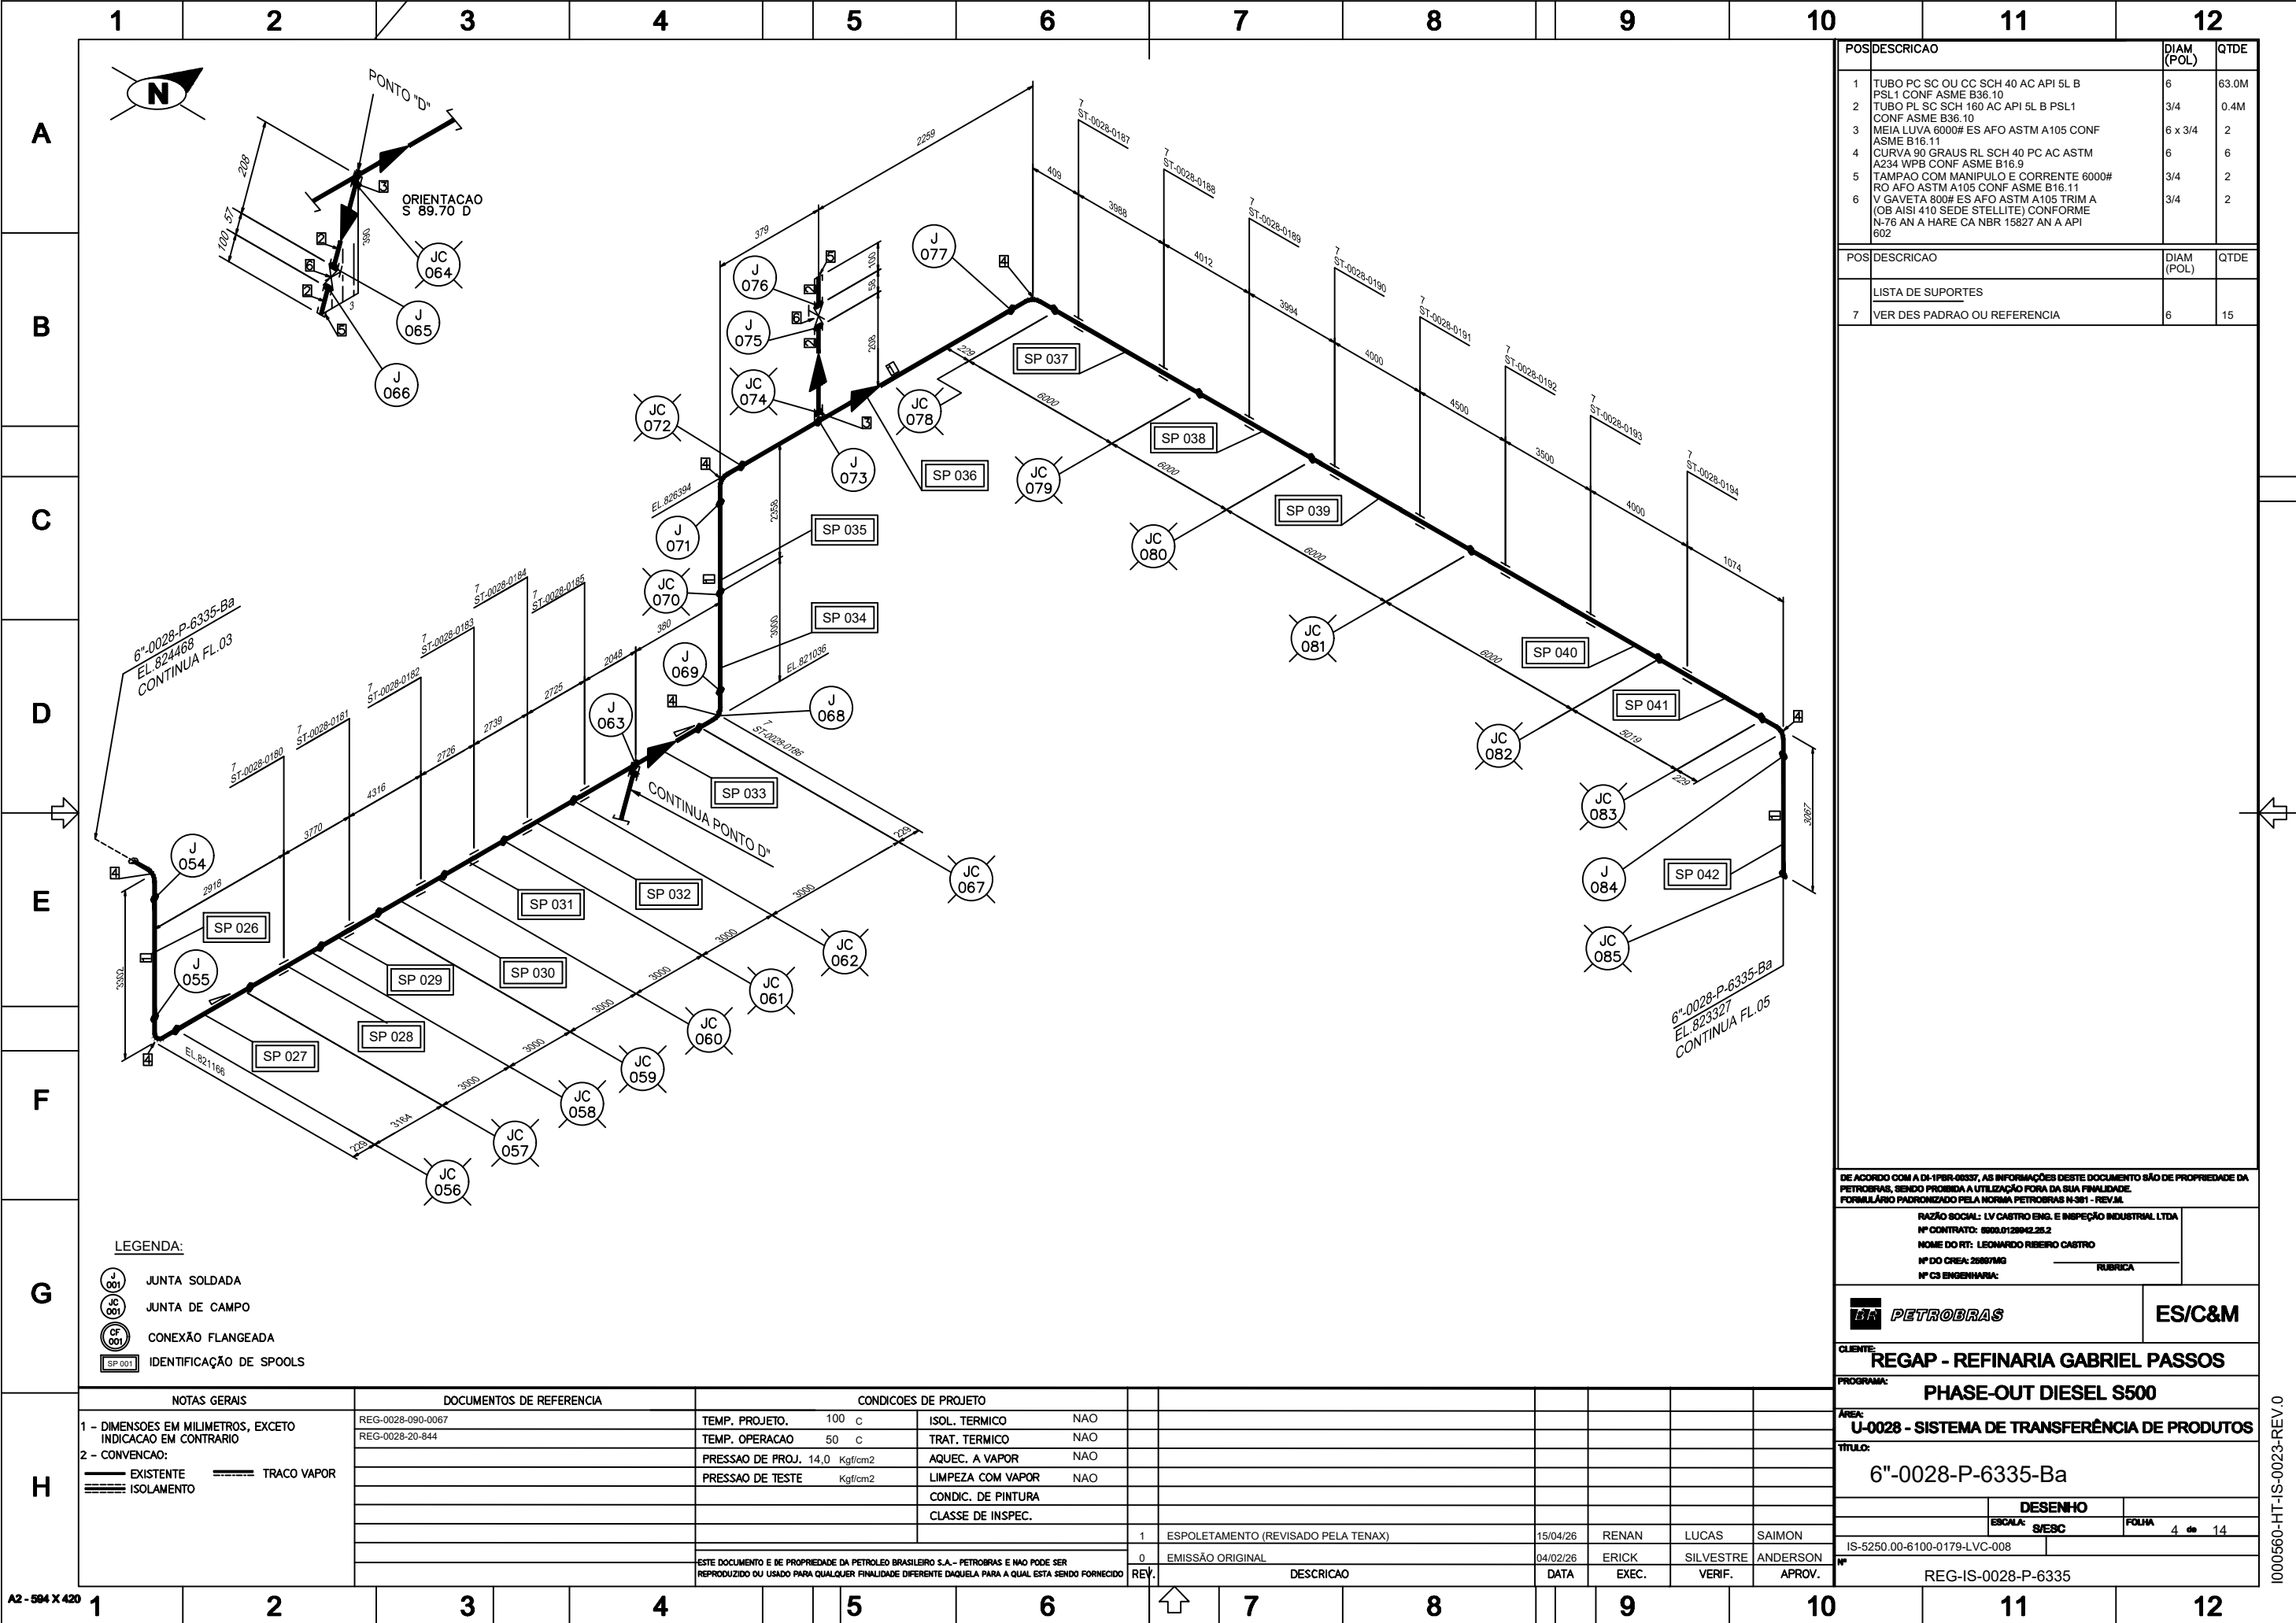

POS	DESCRICAO	DIAM (POL)	QTDE
1	TUBO PC SC OU CC SCH 40 AC API 5L B	6	63.0M
2	PSL1 CONF ASME B36.10	3/4	0.4M
3	TUBO PL SC SCH 160 AC API 5L B PSL1	6 x 3/4	2
4	CONF ASME B36.10	6	6
5	MEIA LUVIA 6000# ES AFO ASTM A105 CONF	3/4	2
6	ASME B16.11	3/4	2

POS	DESCRICAO	DIAM (POL)	QTDE
7	VER DES PADRAO OU REFERENCIA	6	15

DE ACORDO COM A DI-1PR-00337, AS INFORMAÇÕES DESTA DOCUMENTO SÃO DE PROPRIEDADE DA PETROBRAS, SENDO PROIBIDA A UTILIZAÇÃO FORA DA SUA FINALIDADE. FORMULÁRIO PADRONIZADO PELA NORMA PETROBRAS N-301 - REV.01.			
RAZÃO SOCIAL: LV CASTRO ENG. E INSPEÇÃO INDUSTRIAL LTDA			
Nº CONTRATO: 0000.0128942.252			
NOME DO RT: LEONARDO RIBEIRO CASTRO			
Nº DO CREA: 25887/MG			
Nº C3 ENGENHARIA: RUBRICA			
PETROBRAS		ES/C&M	
CLIENTE: REGAP - REFINARIA GABRIEL PASSOS			
PROGRAMA: PHASE-OUT DIESEL S500			
ÁREA: U-0028 - SISTEMA DE TRANSFERÊNCIA DE PRODUTOS			
TÍTULO: 6"-0028-P-6335-Ba			
DESENHO		FOLHA 4 de 14	
ESCALA: S/ESCALA		FOLHA 4 de 14	
IS-5250.00-6100-0179-LVC-008		Nº	
REG-IS-0028-P-6335		Nº	