


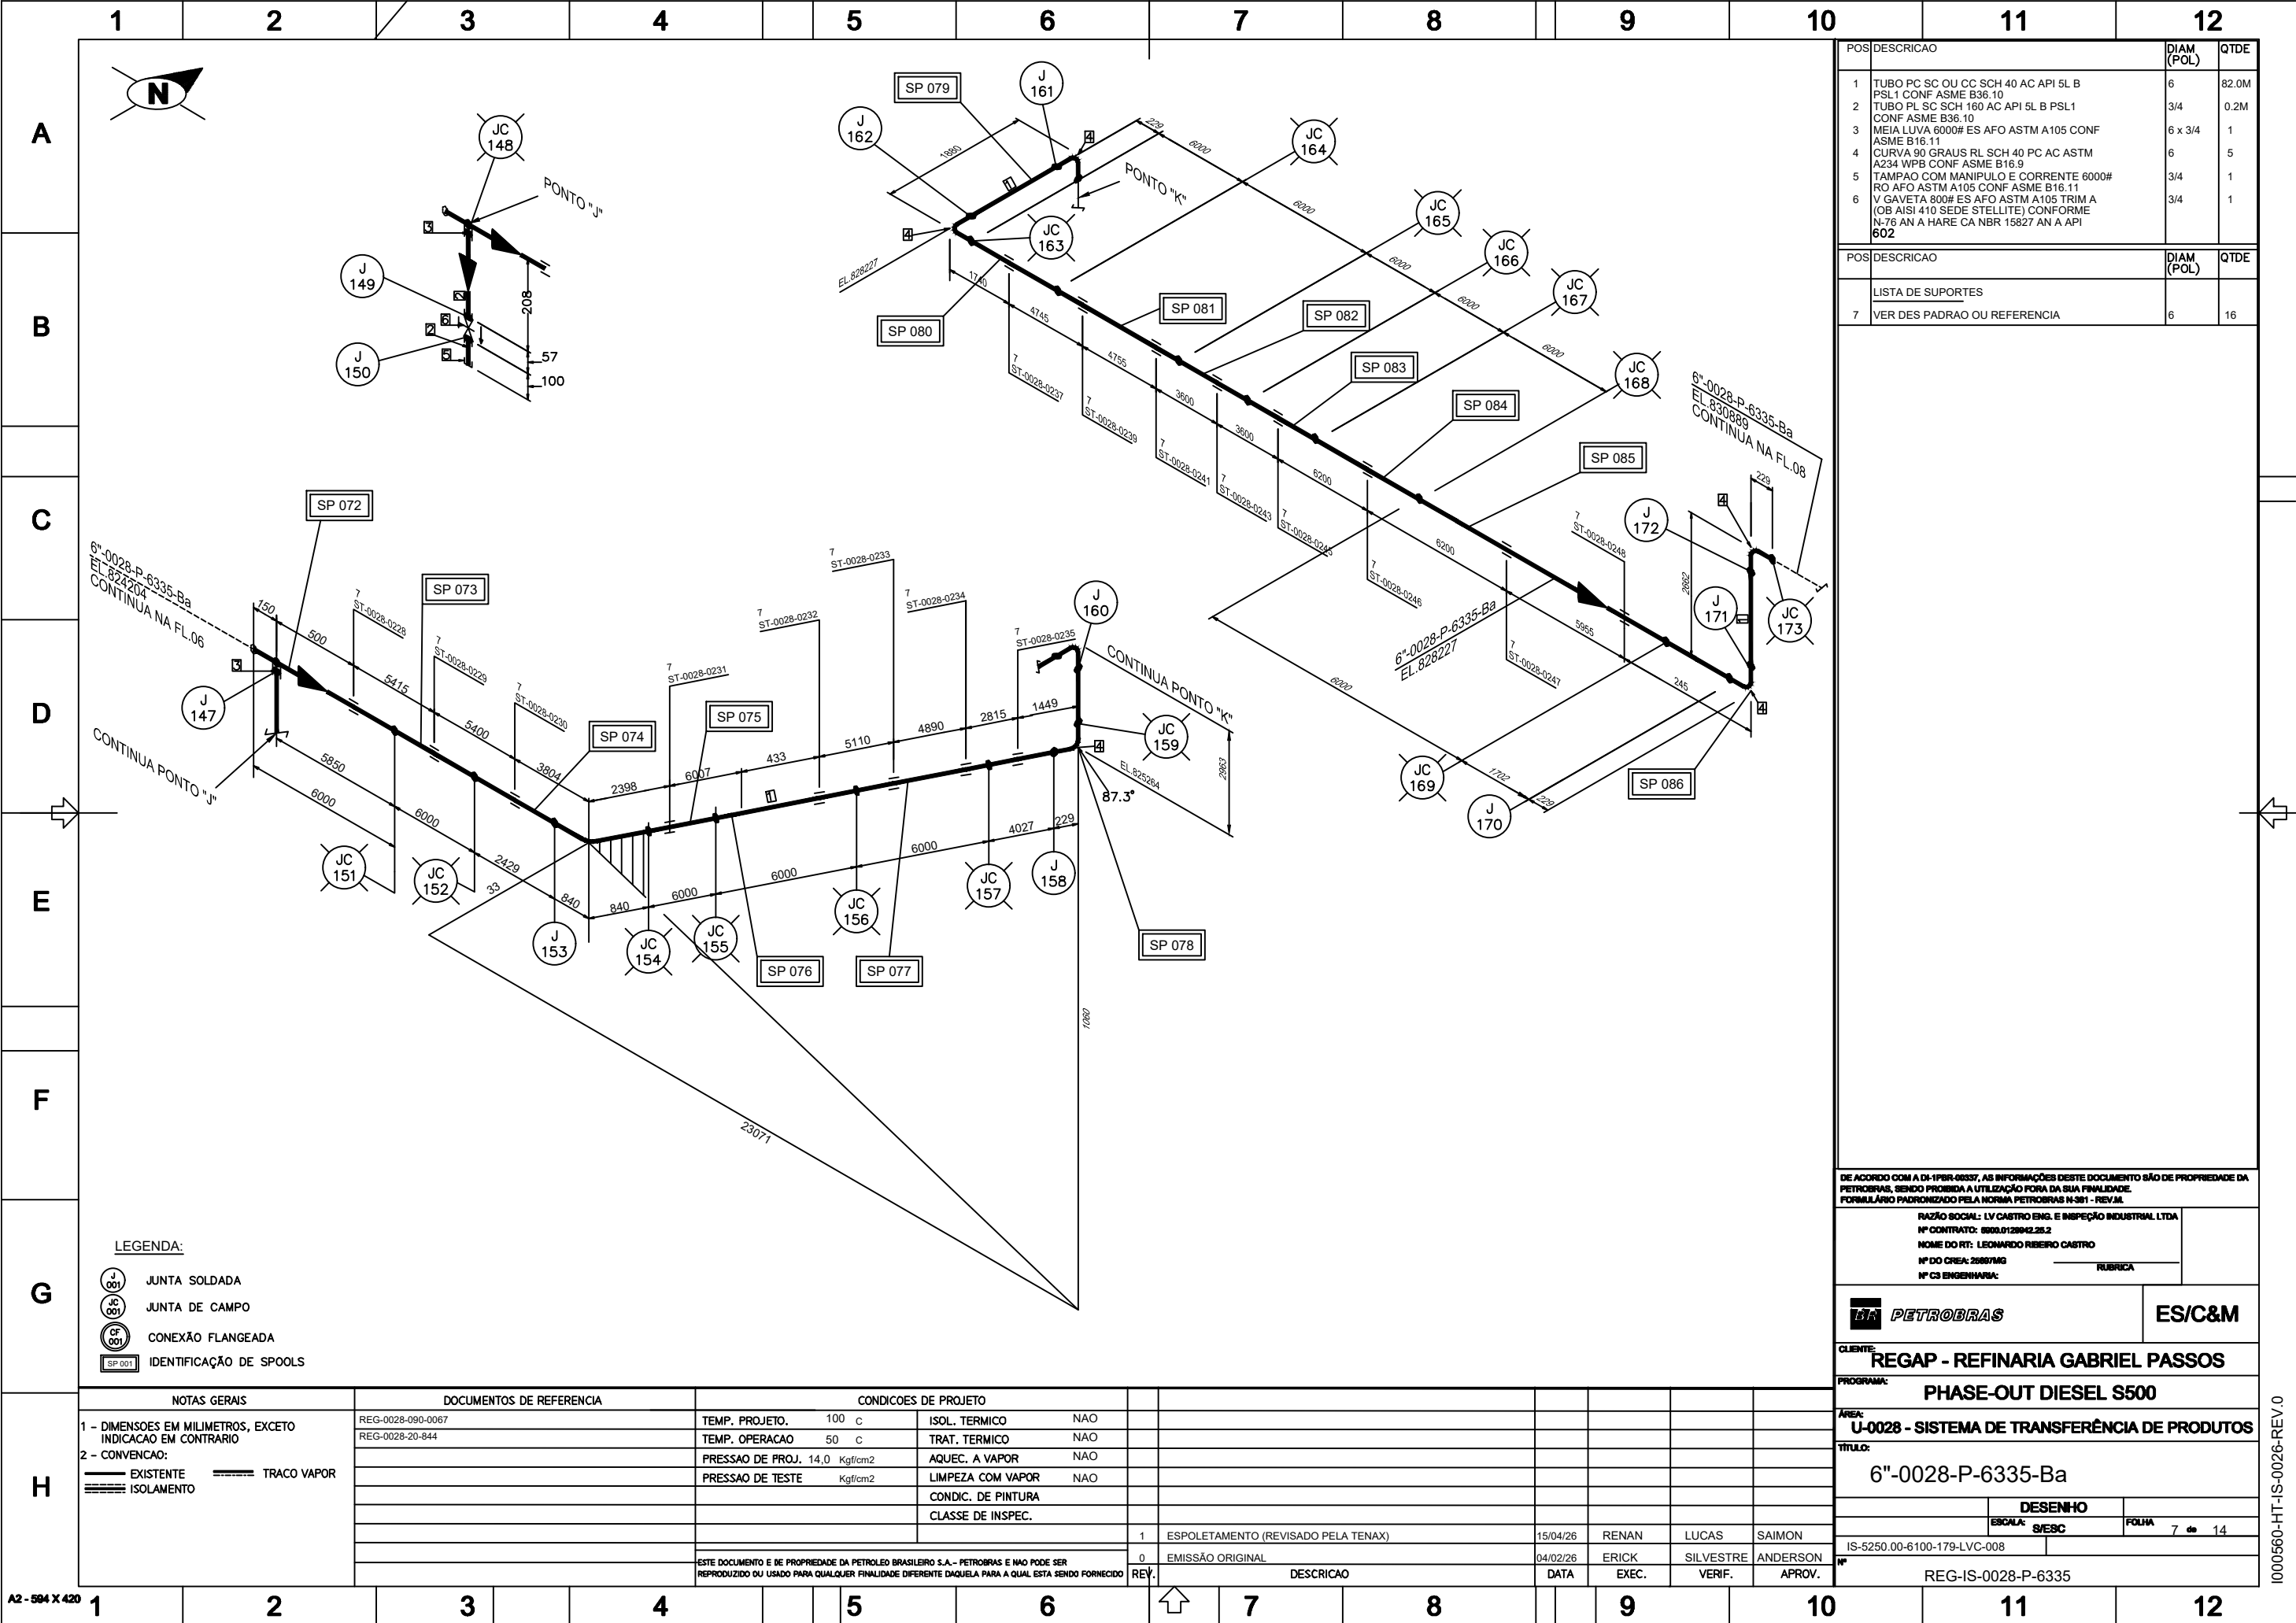

POS	DESCRICAO	DIAM (POL)	QTDE
1	TUBO PC SC OU CC SCH 40 AC API 5L B PSL1 CONF ASME B36.10	6	82.0M
2	TUBO PL SC SCH 160 AC API 5L B PSL1 CONF ASME B36.10	3/4	0.2M
3	MEIA LUVIA 6000# ES AFO ASTM A105 CONF ASME B16.11	6 x 3/4	1
4	CURVA 90 GRAUS RL SCH 40 PC AC ASTM A234 WPB CONF ASME B16.9	6	5
5	TAMPAO COM MANIPULO E CORRENTE 6000# RO AFO ASTM A105 CONF ASME B16.11	3/4	1
6	V GAVETA 800# ES AFO ASTM A105 TRIM A (OB AISI 410 SEDE STELLITE) CONFORME N-76 AN A HARE CA NBR 15827 AN A API 602	3/4	1

POS	DESCRICAO	DIAM (POL)	QTDE
LISTA DE SUPORTES			
7	VER DES PADRAO OU REFERENCIA	6	16

DE ACORDO COM A DI-1PR-00337, AS INFORMAÇÕES DESTES DOCUMENTOS SÃO DE PROPRIEDADE DA PETROBRAS, SENDO PROIBIDA A UTILIZAÇÃO FORA DA SUA FINALIDADE. FORMULÁRIO PADRONIZADO PELA NORMA PETROBRAS N-301 - REV.0

RAZÃO SOCIAL: LV CASTRO ENG. E INSPEÇÃO INDUSTRIAL LTDA	
Nº CONTRATO: 0000.0128942.252	
NOME DO RT: LEONARDO RIBEIRO CASTRO	
Nº DO CREA: 25887/MG	RUBRICA
Nº C3 ENGENHARIA:	

ES/C&M

CLIENTE: **REGAP - REFINARIA GABRIEL PASSOS**

PROGRAMA: **PHASE-OUT DIESEL S500**

ÁREA: **U-0028 - SISTEMA DE TRANSFERÊNCIA DE PRODUTOS**

TÍTULO: **6"-0028-P-6335-Ba**

DESENHO	FOLHA
ESCALA: S/ES	7 de 14

IS-5250.00-6100-179-LVC-008

Nº REG-IS-0028-P-6335