


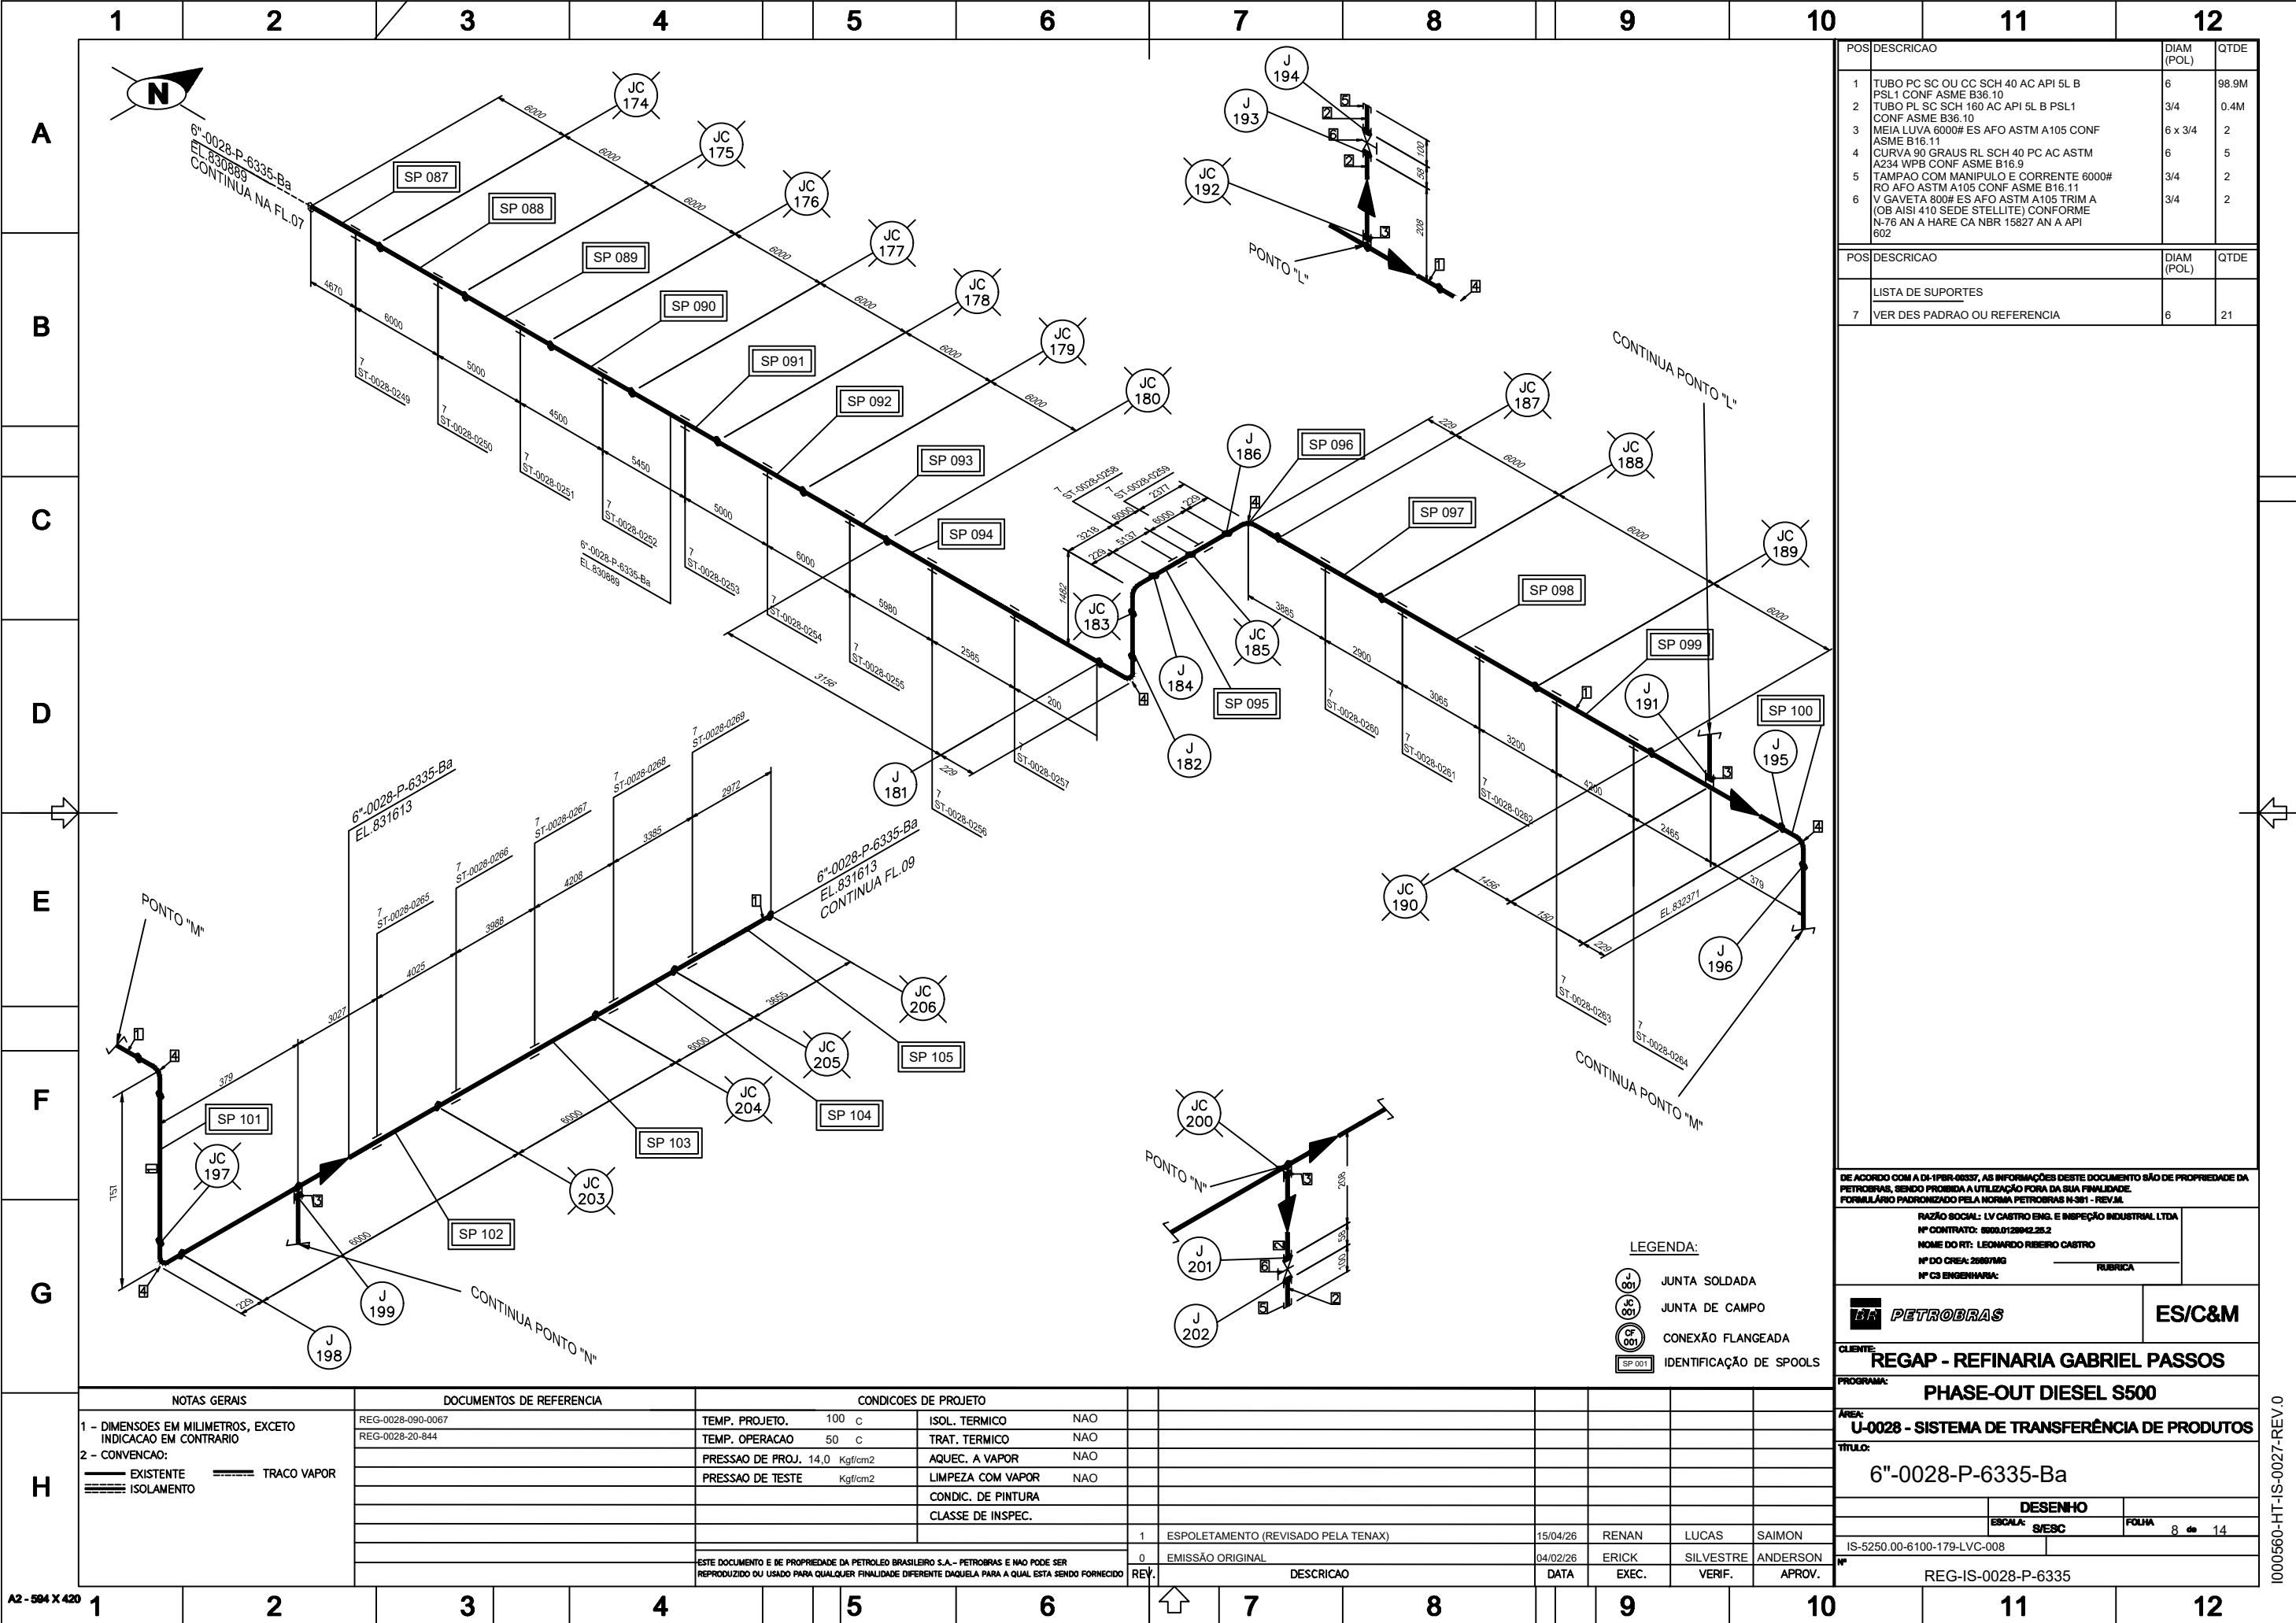

POS	DESCRIÇÃO	DIAM (POL)	QTDE
1	TUBO PC SC OU CC SCH 40 AC API 5L B PSL1 CONF ASME B36.10	6	98.9M
2	TUBO PL SC SCH 160 AC API 5L B PSL1 CONF ASME B36.10	3/4	0.4M
3	MEIA LULA 6000# ES AFO ASTM A105 CONF ASME B16.11	6 x 3/4	2
4	CURVA 90 GRAUS RL SCH 40 PC AC ASTM A234 WPB CONF ASME B16.9	6	5
5	TAMPAO COM MANIPULO E CORRENTE 6000# RO AFO ASTM A105 CONF ASME B16.11	3/4	2
6	V GAVETA 800# ES AFO ASTM A105 TRIM A 10B AISI 410 SEDE STELLITE) CONFORME N-76 AN A HARE CA NBR 15827 AN A API 602	3/4	2

POS	DESCRIÇÃO	DIAM (POL)	QTDE
LISTA DE SUPORTES			
7	VER DES PADRAO OU REFERENCIA	6	21

DE ACORDO COM A DI-1PR-00337, AS INFORMAÇÕES DESTES DOCUMENTOS SÃO DE PROPRIEDADE DA PETROBRAS, SENDO PROIBIDA A UTILIZAÇÃO FORA DA SUA FINALIDADE. FORMULÁRIO PADRONIZADO PELA NORMA PETROBRAS N-301 - REV.M.					
RAZÃO SOCIAL: LV CASTRO ENG. E INSPEÇÃO INDUSTRIAL LTDA					
Nº CONTRATO: 0000.0128942.252					
NOME DO RT: LEONARDO RIBEIRO CASTRO					
Nº DO CREA: 25887/MG					
Nº C3 ENGENHARIA: RUBRICA					
ES/C&M		ES/C&M			
CLIENTE: REGAP - REFINARIA GABRIEL PASSOS					
PROGRAMA: PHASE-OUT DIESEL S500					
ÁREA: U-0028 - SISTEMA DE TRANSFERÊNCIA DE PRODUTOS					
TÍTULO: 6"-0028-P-6335-Ba					
DESENHO		FOLHA 8 de 14			
ESCALA: S/ESCALA		FOLHA 8 de 14			
IS-5250.00-6100-179-LVC-008					
REG-IS-0028-P-6335					

DE ACORDO COM A DI-1PR-00337, AS INFORMAÇÕES DESTES DOCUMENTOS SÃO DE PROPRIEDADE DA PETROBRAS, SENDO PROIBIDA A UTILIZAÇÃO FORA DA SUA FINALIDADE. FORMULÁRIO PADRONIZADO PELA NORMA PETROBRAS N-301 - REV.M.

RAZÃO SOCIAL: LV CASTRO ENG. E INSPEÇÃO INDUSTRIAL LTDA
Nº CONTRATO: 0000.0128942.252
NOME DO RT: LEONARDO RIBEIRO CASTRO
Nº DO CREA: 25887/MG
Nº C3 ENGENHARIA: RUBRICA

ES/C&M

CLIENTE: REGAP - REFINARIA GABRIEL PASSOS

PROGRAMA: PHASE-OUT DIESEL S500

ÁREA: U-0028 - SISTEMA DE TRANSFERÊNCIA DE PRODUTOS

TÍTULO: 6"-0028-P-6335-Ba

DESENHO
ESCALA: S/ESCALA
FOLHA 8 de 14

IS-5250.00-6100-179-LVC-008

REG-IS-0028-P-6335