


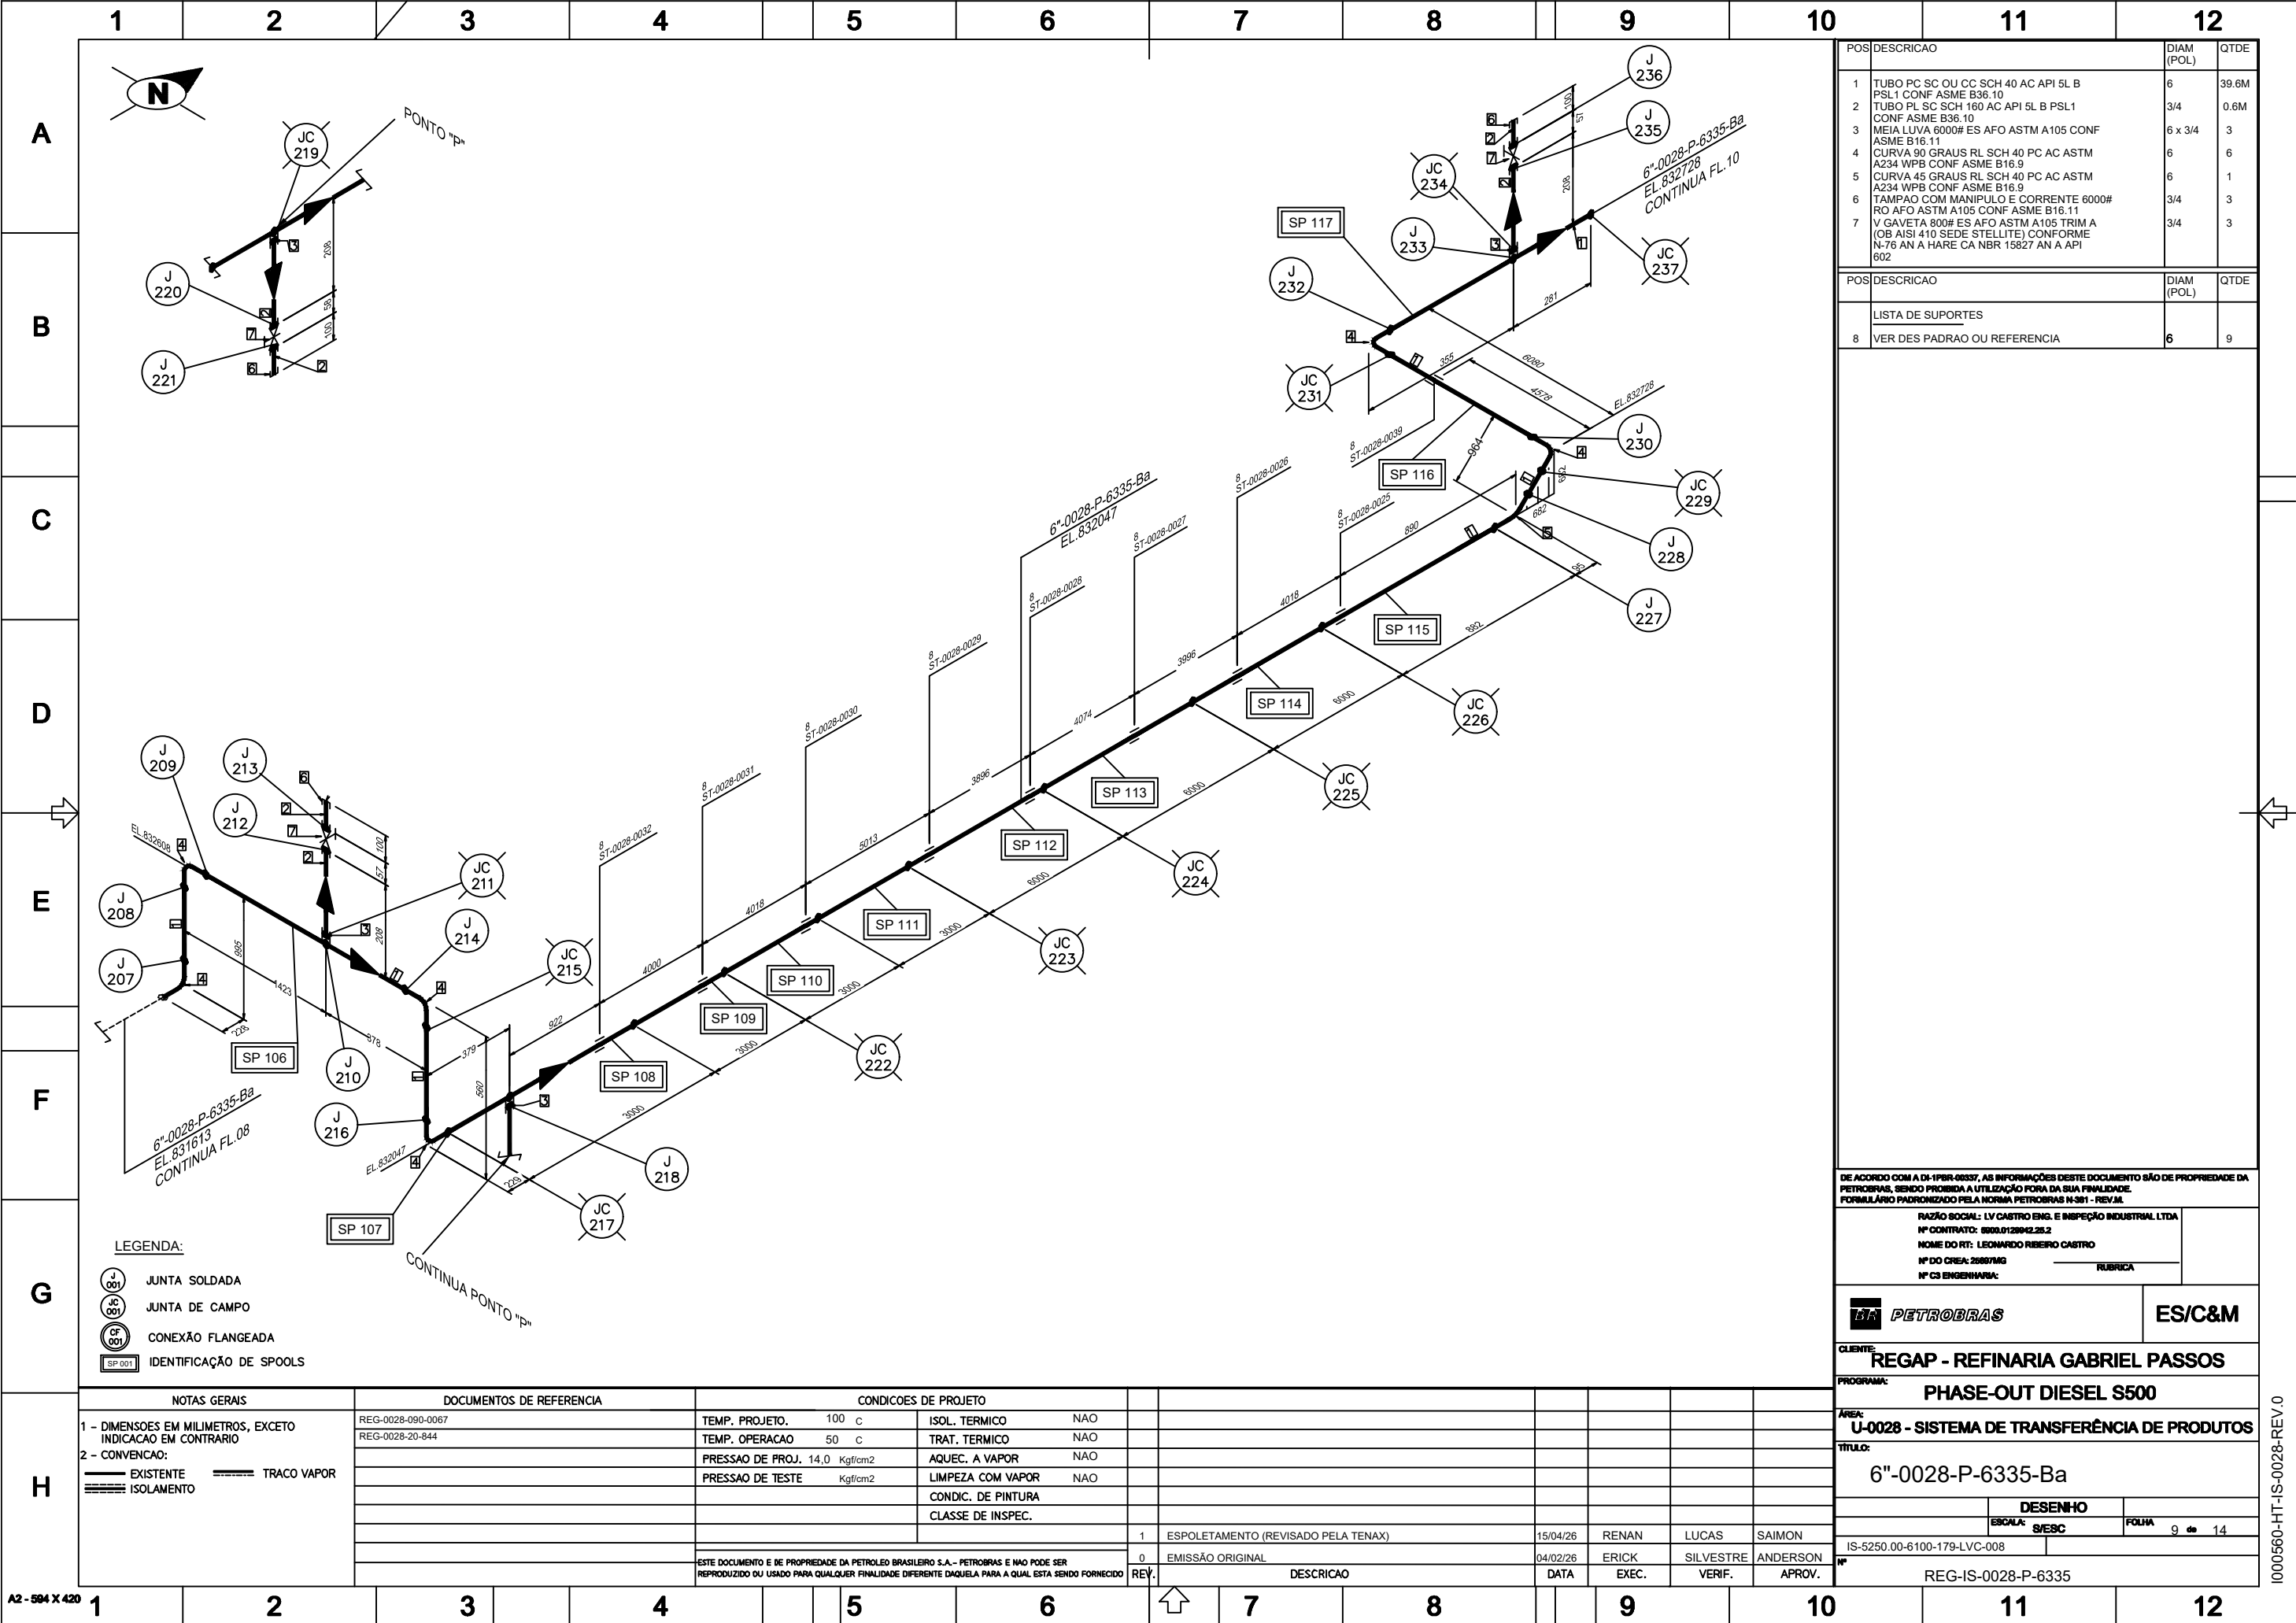

| POS | DESCRIÇÃO   | DIAM (POL) | QTDE  |
|-----|---|------------|-------|
| 1   | TUBO PC SC OU CC SCH 40 AC API 5L B PSL1 CONF ASME B36.10                                                           | 6          | 39.6M |
| 2   | TUBO PL SC SCH 160 AC API 5L B PSL1 CONF ASME B36.10                                                                | 3/4        | 0.6M  |
| 3   | MEIA LULA 6000# ES AFO ASTM A105 CONF ASME B16.11                                                                   | 6 x 3/4    | 3     |
| 4   | CURVA 90 GRAUS RL SCH 40 PC AC ASTM A234 WPB CONF ASME B16.9                                                        | 6          | 6     |
| 5   | CURVA 45 GRAUS RL SCH 40 PC AC ASTM A234 WPB CONF ASME B16.9                                                        | 6          | 1     |
| 6   | TAMPAO COM MANIPULO E CORRENTE 6000# RO AFO ASTM A105 CONF ASME B16.11                                              | 3/4        | 3     |
| 7   | V GAVETA 800# ES AFO ASTM A105 TRIM A (08 AISI 410 SEDE STELLITE) CONFORME N-76 AN A HARE CA NBR 15827 AN A API 602 | 3/4        | 3     |

| POS               | DESCRIÇÃO                    | DIAM (POL) | QTDE |
|-------------------|------------------------------|------------|------|
| LISTA DE SUPORTES |                              |            |      |
| 8                 | VER DES PADRAO OU REFERENCIA | 6          | 9    |

DE ACORDO COM A DI-1PR-00337, AS INFORMAÇÕES DESTA DOCUMENTO SÃO DE PROPRIEDADE DA PETROBRAS, SENDO PROIBIDA A UTILIZAÇÃO FORA DA SUA FINALIDADE. FORMULÁRIO PADRONIZADO PELA NORMA PETROBRAS N-301 - REV.01.

|                                                         |         |
|---------------------------------------------------------|---------|
| RAZÃO SOCIAL: LV CASTRO ENG. E INSPEÇÃO INDUSTRIAL LTDA |         |
| Nº CONTRATO: 0000.0128942.252                           |         |
| NOME DO RT: LEONARDO RIBEIRO CASTRO                     |         |
| Nº DO CREA: 25887/MG                                    | RUBRICA |
| Nº C3 ENGENHARIA:                                       |         |

|           |        |
|-----------|--------|
| PETROBRAS | ES/C&M |
|-----------|--------|

CLIENTE: **REGAP - REFINARIA GABRIEL PASSOS**

PROGRAMA: **PHASE-OUT DIESEL S500**

ÁREA: **U-0028 - SISTEMA DE TRANSFERÊNCIA DE PRODUTOS**

TÍTULO: **6"-0028-P-6335-Ba**

|              |         |         |
|--------------|---------|---------|
|              | DESENHO |         |
| ESCALA: S/ES | FOLHA   | 9 de 14 |

IS-5250.00-6100-179-LVC-008

Nº REG-IS-0028-P-6335