


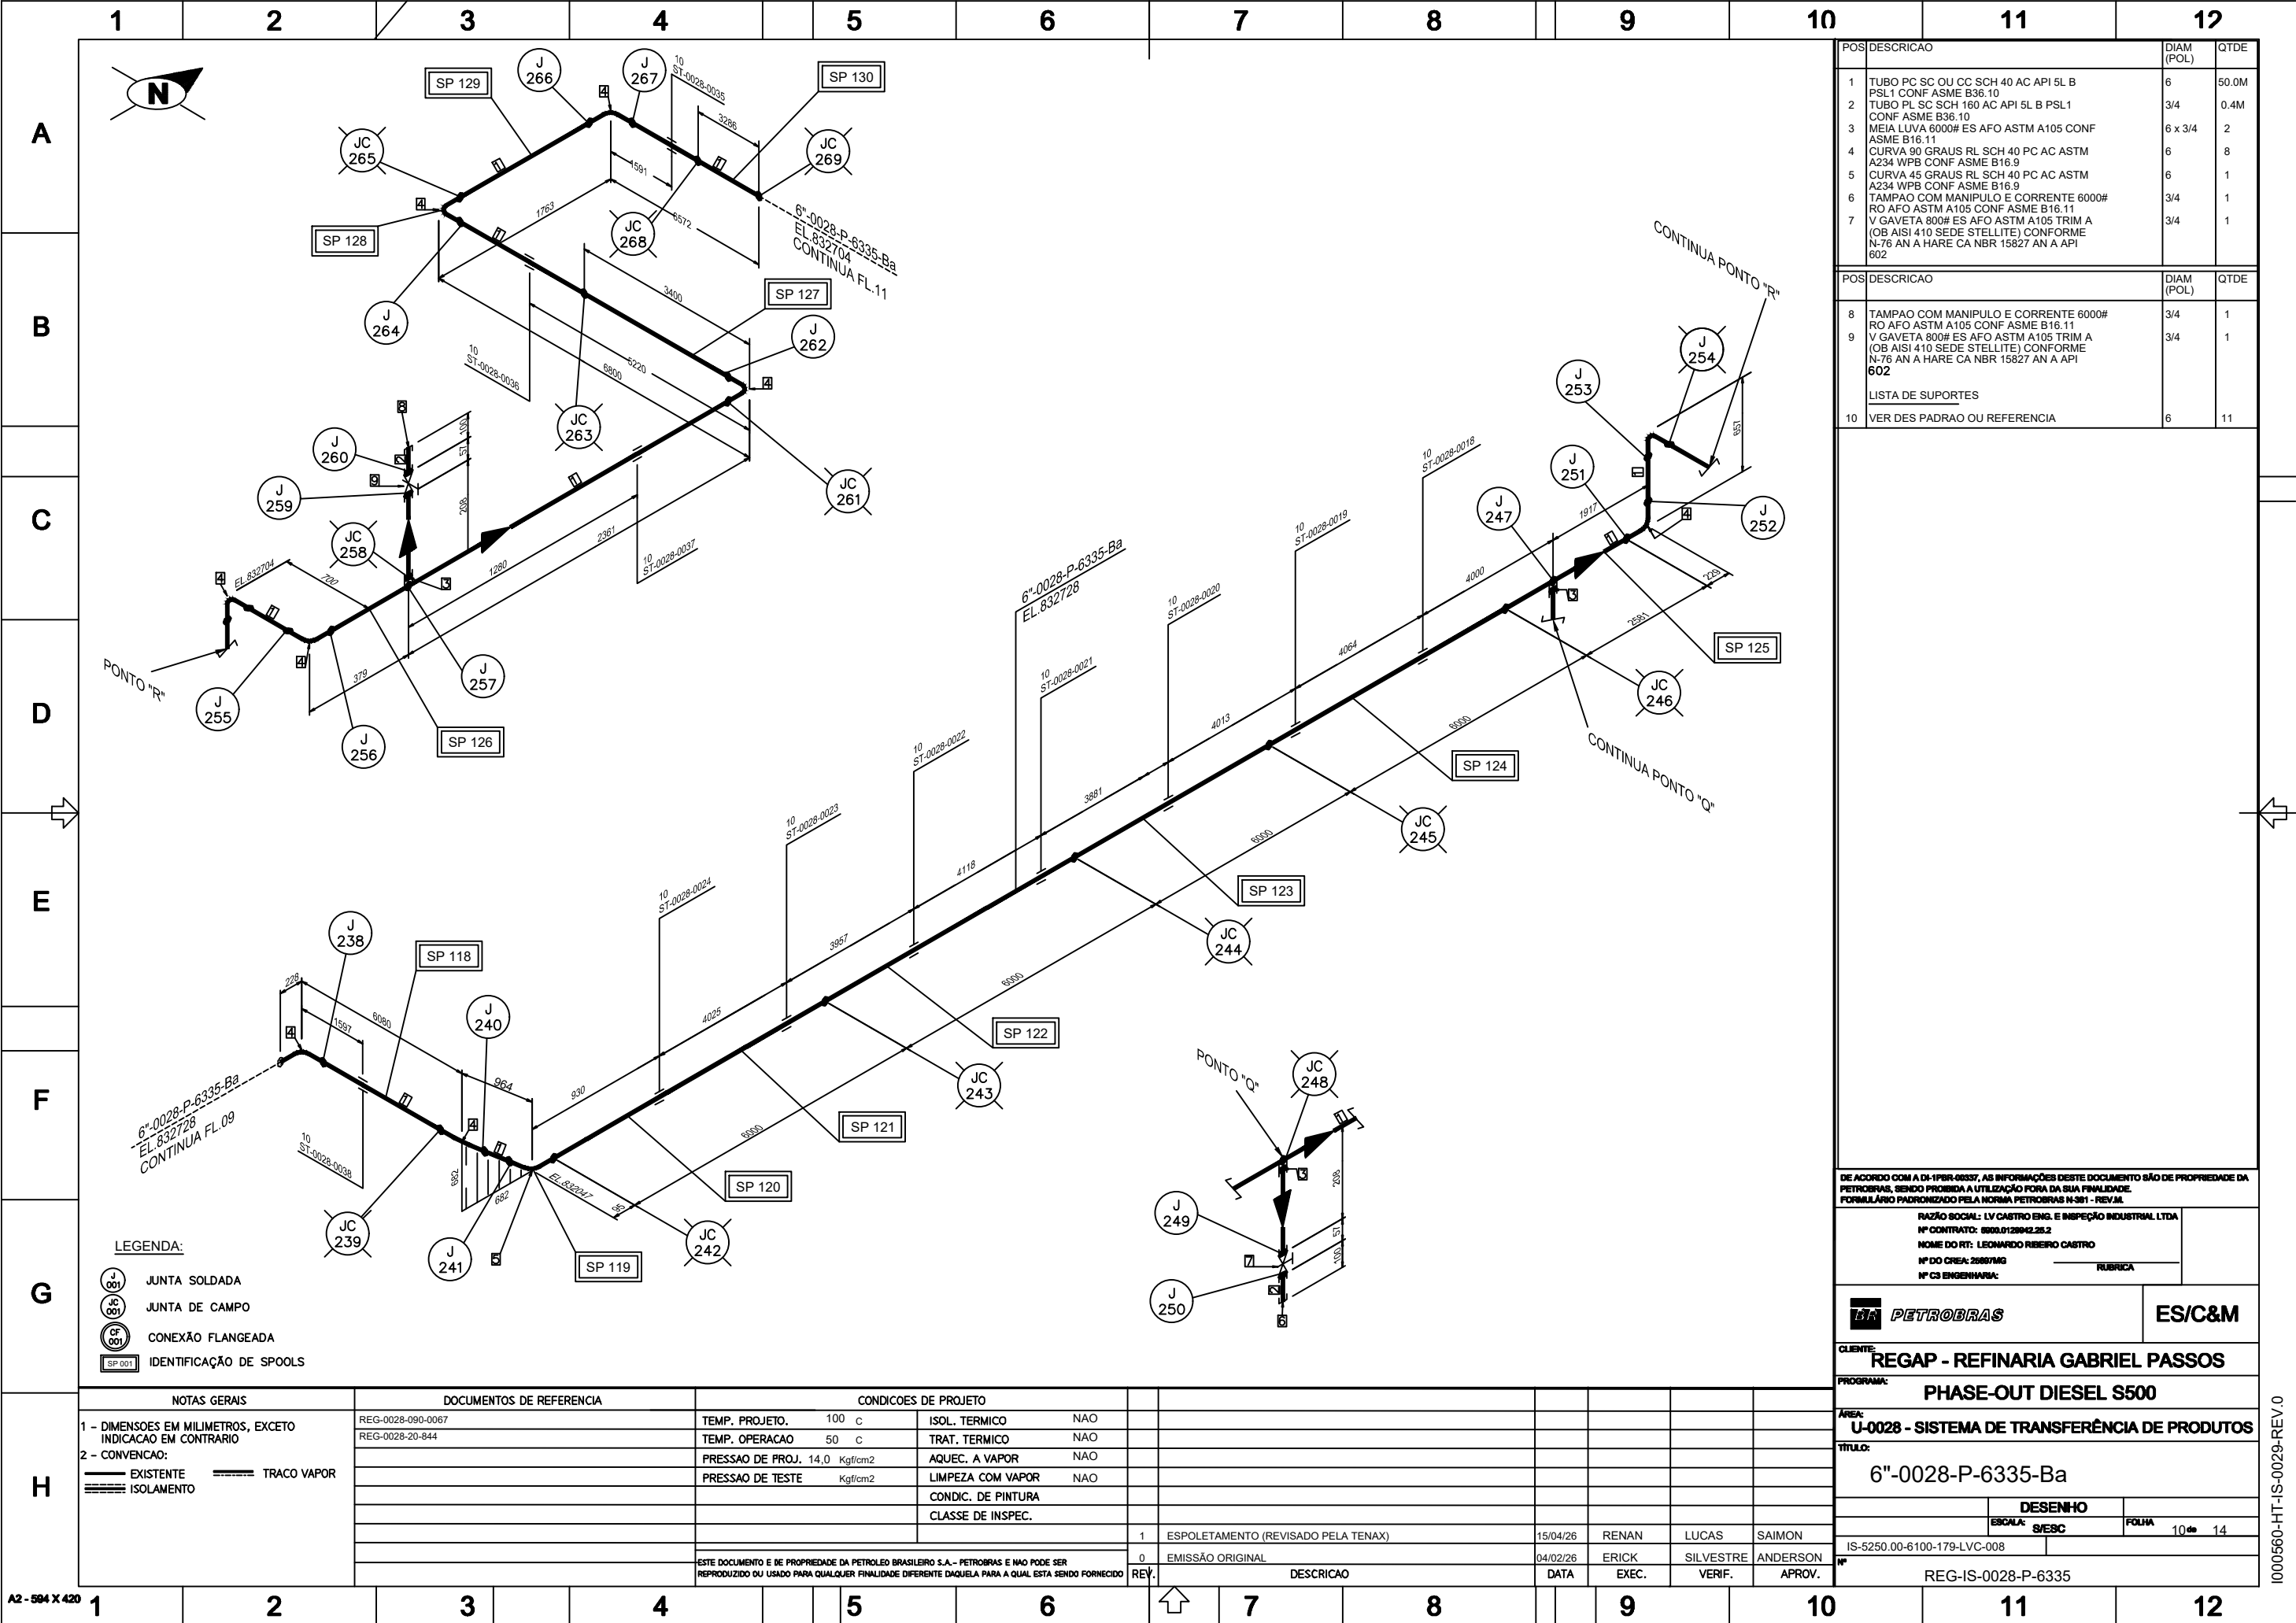

POS	DESCRICAO	DIAM (POL)	QTDE
1	TUBO PC SC OU CC SCH 40 AC API 5L B PSL1 CONF ASME B36.10	6	50.0M
2	TUBO PL SC SCH 160 AC API 5L B PSL1 CONF ASME B36.10	3/4	0.4M
3	MEIA LULA 6000# ES AFO ASTM A105 CONF ASME B16.11	6 x 3/4	2
4	CURVA 90 GRAUS RL SCH 40 PC AC ASTM A234 WPB CONF ASME B16.9	6	8
5	CURVA 45 GRAUS RL SCH 40 PC AC ASTM A234 WPB CONF ASME B16.9	6	1
6	TAMPAO COM MANIPULO E CORRENTE 6000# RO AFO ASTM A105 CONF ASME B16.11	3/4	1
7	V GAVETA 800# ES AFO ASTM A105 TRIM A (OB AISI 410 SEDE STELLITE) CONFORME N-76 AN A HARE CA NBR 15827 AN A API 602	3/4	1

POS	DESCRICAO	DIAM (POL)	QTDE
8	TAMPAO COM MANIPULO E CORRENTE 6000# RO AFO ASTM A105 CONF ASME B16.11	3/4	1
9	V GAVETA 800# ES AFO ASTM A105 TRIM A (OB AISI 410 SEDE STELLITE) CONFORME N-76 AN A HARE CA NBR 15827 AN A API 602	3/4	1
10	VER DES PADRAO OU REFERENCIA	6	11

LISTA DE SUPORTES			
VER DES PADRAO OU REFERENCIA			

DE ACORDO COM A DI-1PR-00337, AS INFORMAÇÕES DESTA DOCUMENTAÇÃO SÃO DE PROPRIEDADE DA PETROBRAS, SENDO PROIBIDA A UTILIZAÇÃO FORA DA SUA FINALIDADE. FORMULÁRIO PADRONIZADO PELA NORMA PETROBRAS N-301 - REV.01.

RAZÃO SOCIAL: LV CASTRO ENG. E INSPEÇÃO INDUSTRIAL LTDA
Nº CONTRATO: 0000.0128942.252
NOME DO RT: LEONARDO RIBEIRO CASTRO
Nº DO CREA: 25887/MG
Nº C3 ENGENHARIA: RUBRICA

ES/C&M

CLIENTE: **REGAP - REFINARIA GABRIEL PASSOS**

PROGRAMA: **PHASE-OUT DIESEL S500**

ÁREA: **U-0028 - SISTEMA DE TRANSFERÊNCIA DE PRODUTOS**

TÍTULO: **6"-0028-P-6335-Ba**

DESENHO
ESCALA: S/ESCALA
FOLHA 10 de 14

IS-5250.00-6100-179-LVC-008

REG-IS-0028-P-6335